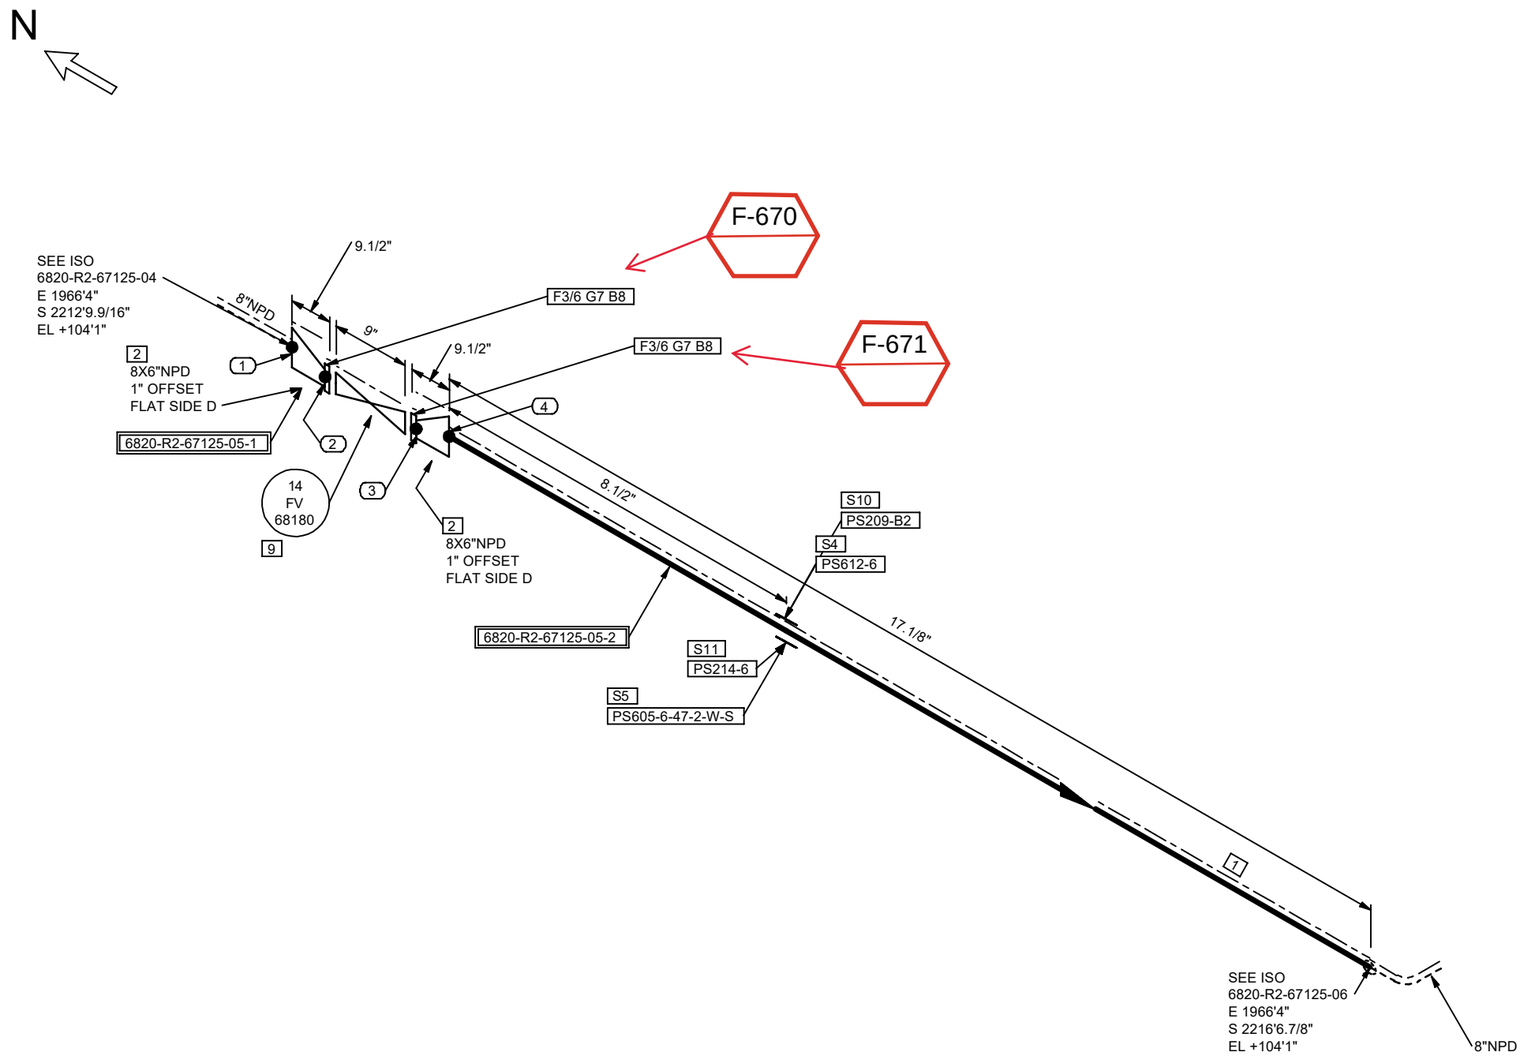


SHOP MATERIALS

NO	NPD	DESCRIPTION	IDENT	QTY
1	8	Pipes, Seamless, ASME B36.19/B36.10, ASTM A312 Gr.TP316L, BE, -, -, S-10S	CPPFEGLE	1.5 '
2	8X6	Ecc Reducer, Seamless, ASME B16.9, ASTM A403 Gr.WP316L, BW Ends, -,Annealed, S-10S	C6SDRNRM	2
3	6	LJ Flg, ASME B16.5, ASTM A105 Galv. as per ASTM A153, 150 Lbs, FF, -,	C26WFFFP	2
		PIPE SUPPORTS		
4	8	PS612-6	PS612	1
5	8	PS605-6-47-2-W-S	PS605	1
		MISCELLANEOUS COMPONENTS		
6	6	Stub SP, Seamless, ASME B16.9, ASTM A403 Gr.WP316L, BW Ends, -,Annealed, x S-10S	C8A57S2C	2

OTHER THAN SHOP MATERIALS

NO	NPD	DESCRIPTION	IDENT	QTY
7	6	NM Flat Gk, Barium Sulfate filled PTFE, 150 Lbs, RF as per ASME B16.5, -, Thk=1/8in, -,	C6S4K87R	2
8	3/4	SBlt 2 HHx N, A193 Gr.B7/A194 Gr.2H, -, Xylan PTFE Coated, - 4.25 in. Length	C6S4K8BC	16
		INSTRUMENTS		
9	6	14-FV-68180	14-FV-68180	1
		PIPE SUPPORTS		
10	8	PS209-B2	PS209	1
11	8	PS214-6	PS214	1

PIECE MARKS

6820-R2-67125-05-1 6820-R2-67125-05-2

Filler Material Requisition

Date: 7-16-24

Line Class: NOHD-SS01

WPS: N/A

Electrode: NO FIELD WELDS

Signature: Pedro Morin

COORDINATE SYSTEM : PLANTCOORDINATES

Turner Industries Group, LLC
Received
July 16,2024
DOCUMENT CONTROL

NOTES:

1. FOR LINE PRESSURES, TEMPERATURES, INSULATION TYPE AND THICKNESS, ETC. REFER TO LATEST REVISION OF LDT.
2. FOR STANDARD PIPE SUPPORT DETAILS SEE PROJECT STANDARD.
3. FIELD SHIM TO SUIT UNLESS OTHERWISE NOTED.
4. FOR PWHT REQUIREMENTS REFER TO LINE CLASS SPECIFICATION.
5. ALL THREADED PIPE LINE SYSTEMS, FIELD SHALL VERIFY DIMENSION PRIOR TO ERECTION.
6. FFW DESIGNATION AT WELDS INDICATES FIELD FIT WELD, WHERE PIPE FABRICATOR IS TO ADD 9 INCH OF PIPE TO THE ISOMETRIC DIMENSION TO ENABLE THE FIELD TO CUT TO FIT AT SITE.
7. REFER TO 202998C-000-W1-1300-0001 FOR FRP AND DUAL-LAM FABRICATION.

T.EN TECHNIP ENERGIES

information contained in this document is the work product of one or more legal entities of Technip Energies N.V. and embodies confidential and proprietary information of the applicable entity and/or its client.use of this information is restricted in accordance with conditions specified by the contract.Technip Energies N.V. and its affiliates disclaim any and all liabilities for any changes or modifications to this document which are made by any person other than the entity that issued the document under the applicable client contract.

THIS DOCUMENT IS UNCONTROLLED WHEN REPRODUCED

REV	DATE	BY	DESCRIPTION	CHKD	MTO	STRESS	APRVD
0	2024-07-13	RVA	ISSUED FOR CONSTRUCTION	SAD	KJK	BRD	GR

SERVICE:	VAPOR/LIQUID:	INSUL TYPE:	INSUL THK:	SHOP:	FIELD:	PAINT CODE:	MODULE:
R2	L	Per LDT	Per LDT	Y	Y	Per LDT	-

OXY

OxyChem Redstone Battleground
PROJECT

P&ID: 202998C-001-PID-0021-0328

UNIT#:	EWP AREA:	SPEC:	STRESS CALC #:
6800	6820	NOHD-SS01	CN-0392

LINE No.: 8"-R2-67125-NOHD-SS01-HET

DRAWING NUMBER: **6820-R2-67125-05**

REV.: **0**

13 JUL 2024 11:29