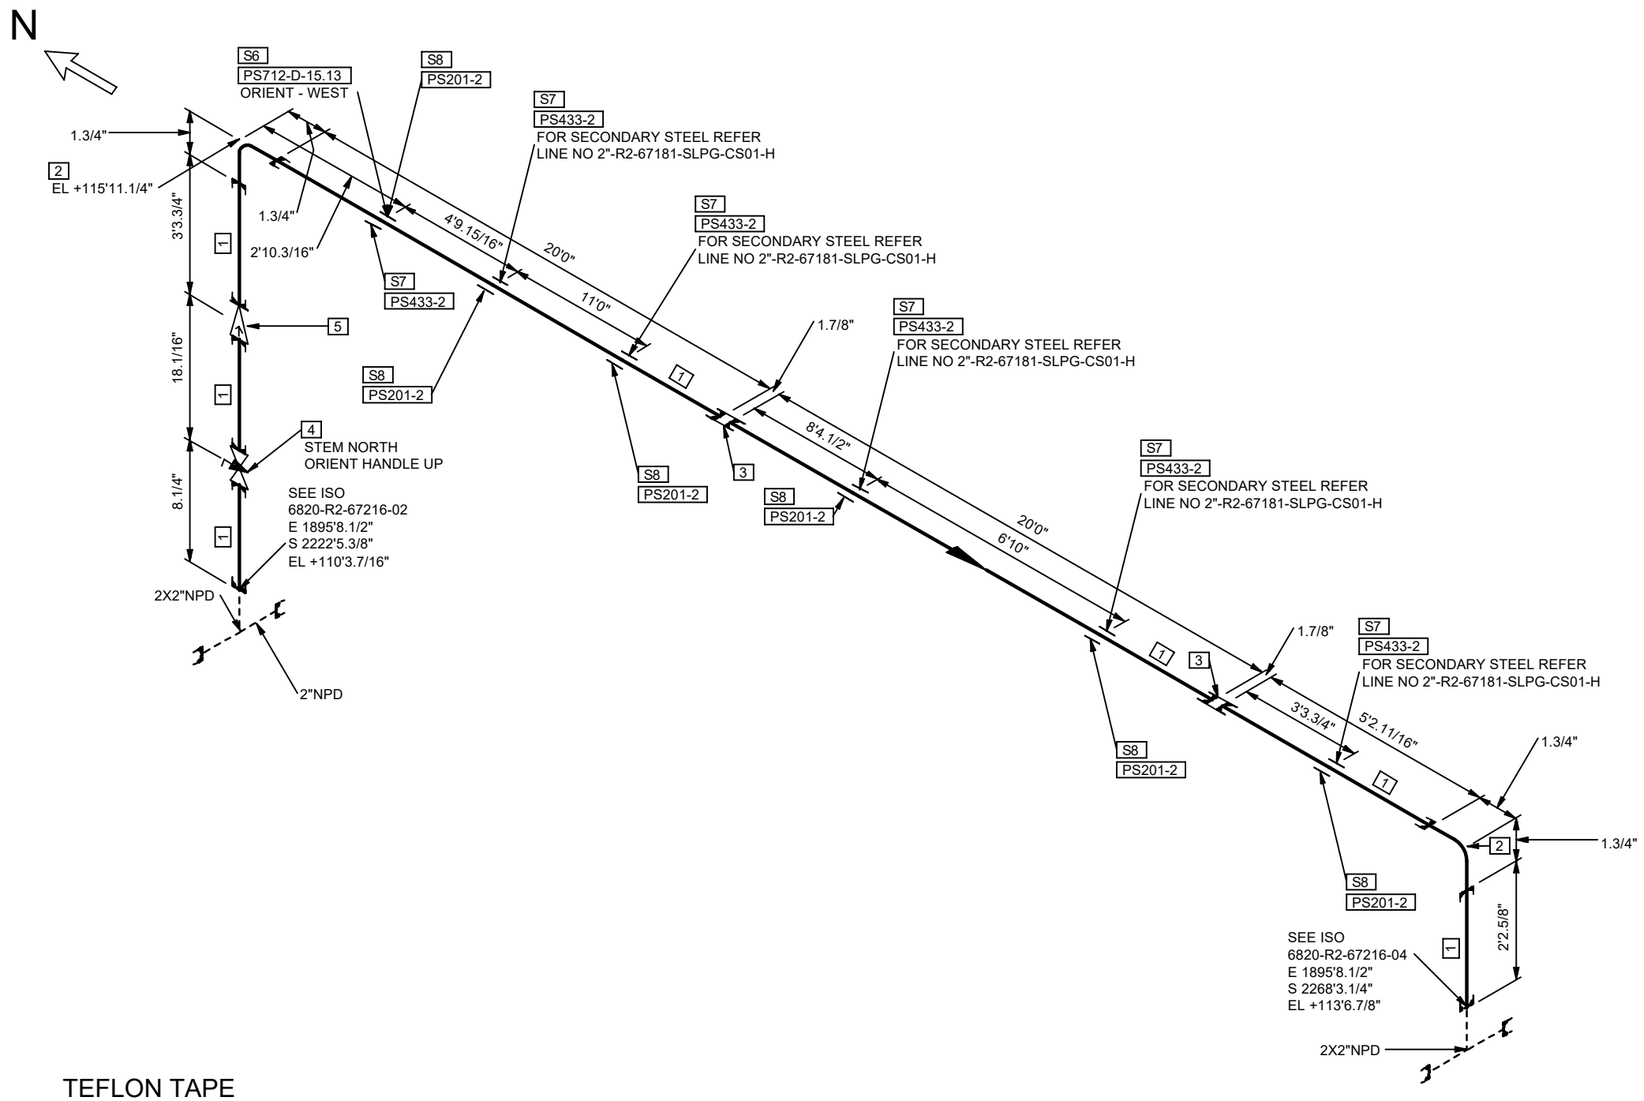


OTHER THAN SHOP MATERIALS

NO	NPD	DESCRIPTION	IDENT	QTY
1	2	Pipes, Seamless, ASME B36.10, ASTM A53 Gr.B Galv. as per ASTM A153, NPTM Ends, w/ coupling, -, S-XS	C8GWJY7T	52.3 '
2	2	90° Elb, ASME B16.11, ASTM A105N Galv. as per ASTM A153, 3000 Lbs, NPTF Ends, -,	C1DMWEN	2
3	2	Full Coup, ASME B16.11, ASTM A105N Galv. as per ASTM A153, 3000 Lbs, NPTF Ends, -,	CZ2LEZH	2
4	2	Plug Fem,RgP, Tapered Plug, Non Lubricated, API 599, ASTM A395 Gr.60-40-18, 300 Lbs, NPTF Ends, Ends as per ASME B16.11,-, LO, -, Valve Tag: PL-0545	C76S9AH4	1
5	2	SwgChk Y Fem,MSS SP-80,ASTM B61 UNS C92200,NPTF Ends,200 Lbs, Valve Tag: CH-0171	C766B01H	1
		PIPE SUPPORTS		
6	2	PS712-D-15.13	PS712	1
7	2	PS433-2	PS433	6
8	2	PS201-2	PS201	6

TEFLON TAPE

Filler Material Requisition

Date: 3-5-25

Line Class: ARWW-XX01

WPS: N/A

Electrode: N/A

Signature: _____

COORDINATE SYSTEM : PLANTCOORDINATES

Turner Industries Group, LLC
Received
MARCH 4, 2025
DOCUMENT CONTROL

NOTES:

1. FOR LINE PRESSURES, TEMPERATURES, INSULATION TYPE AND THICKNESS, ETC. REFER TO LATEST REVISION OF LDT.
2. FOR STANDARD PIPE SUPPORT DETAILS SEE PROJECT STANDARD.
3. FIELD SHIM TO SUIT UNLESS OTHERWISE NOTED.
4. FOR PWHT REQUIREMENTS REFER TO LINE CLASS SPECIFICATION.
5. ALL THREADED PIPE LINE SYSTEMS, FIELD SHALL VERIFY DIMENSION PRIOR TO ERECTION.
6. FFW DESIGNATION AT WELDS INDICATES FIELD FIT WELD, WHERE PIPE FABRICATOR IS TO ADD 9 INCH OF PIPE TO THE ISOMETRIC DIMENSION TO ENABLE THE FIELD TO CUT TO FIT AT SITE.
7. REFER TO 202998C-000-W1-1300-0001 FOR FRP AND DUAL-LAM FABRICATION.

T.EN TECHNIP ENERGIES

information contained in this document is the work product of one or more legal entities of Technip Energies N.V. and embodies confidential and proprietary information of the applicable entity and/or its client.use of this information is restricted in accordance with conditions specified by the contract.Technip Energies N.V. and its affiliates disclaim any and all liabilities for any changes or modifications to this document which are made by any person other than the entity that issued the document under the applicable client contract.

THIS DOCUMENT IS UNCONTROLLED WHEN REPRODUCED

REV	DATE	BY	DESCRIPTION	CHKD	MTO	STRESS	APRVD
0	2025-02-28	RVA	ISSUED FOR CONSTRUCTION	SAD	KJK	SMR	GR

SERVICE:	VAPOR/LIQUID:	INSUL TYPE:	INSUL THK:	SHOP:	FIELD:	PAINT CODE:	MODULE:
R2	V	Per LDT	Per LDT	N	Y	Per LDT	-

OXY

OxyChem Redstone Battleground
PROJECT

P&ID: 202998C-001-PID-0031-0967

UNIT#:	EWP AREA:	SPEC:	STRESS CALC #:
6800	6820	ARWW-XX01	-

LINE No. 2"-R2-67216-ARWW-XX01-N

DRAWING NUMBER 6820-R2-67216-03

REV. 0

01 MAR 2025 07:02